


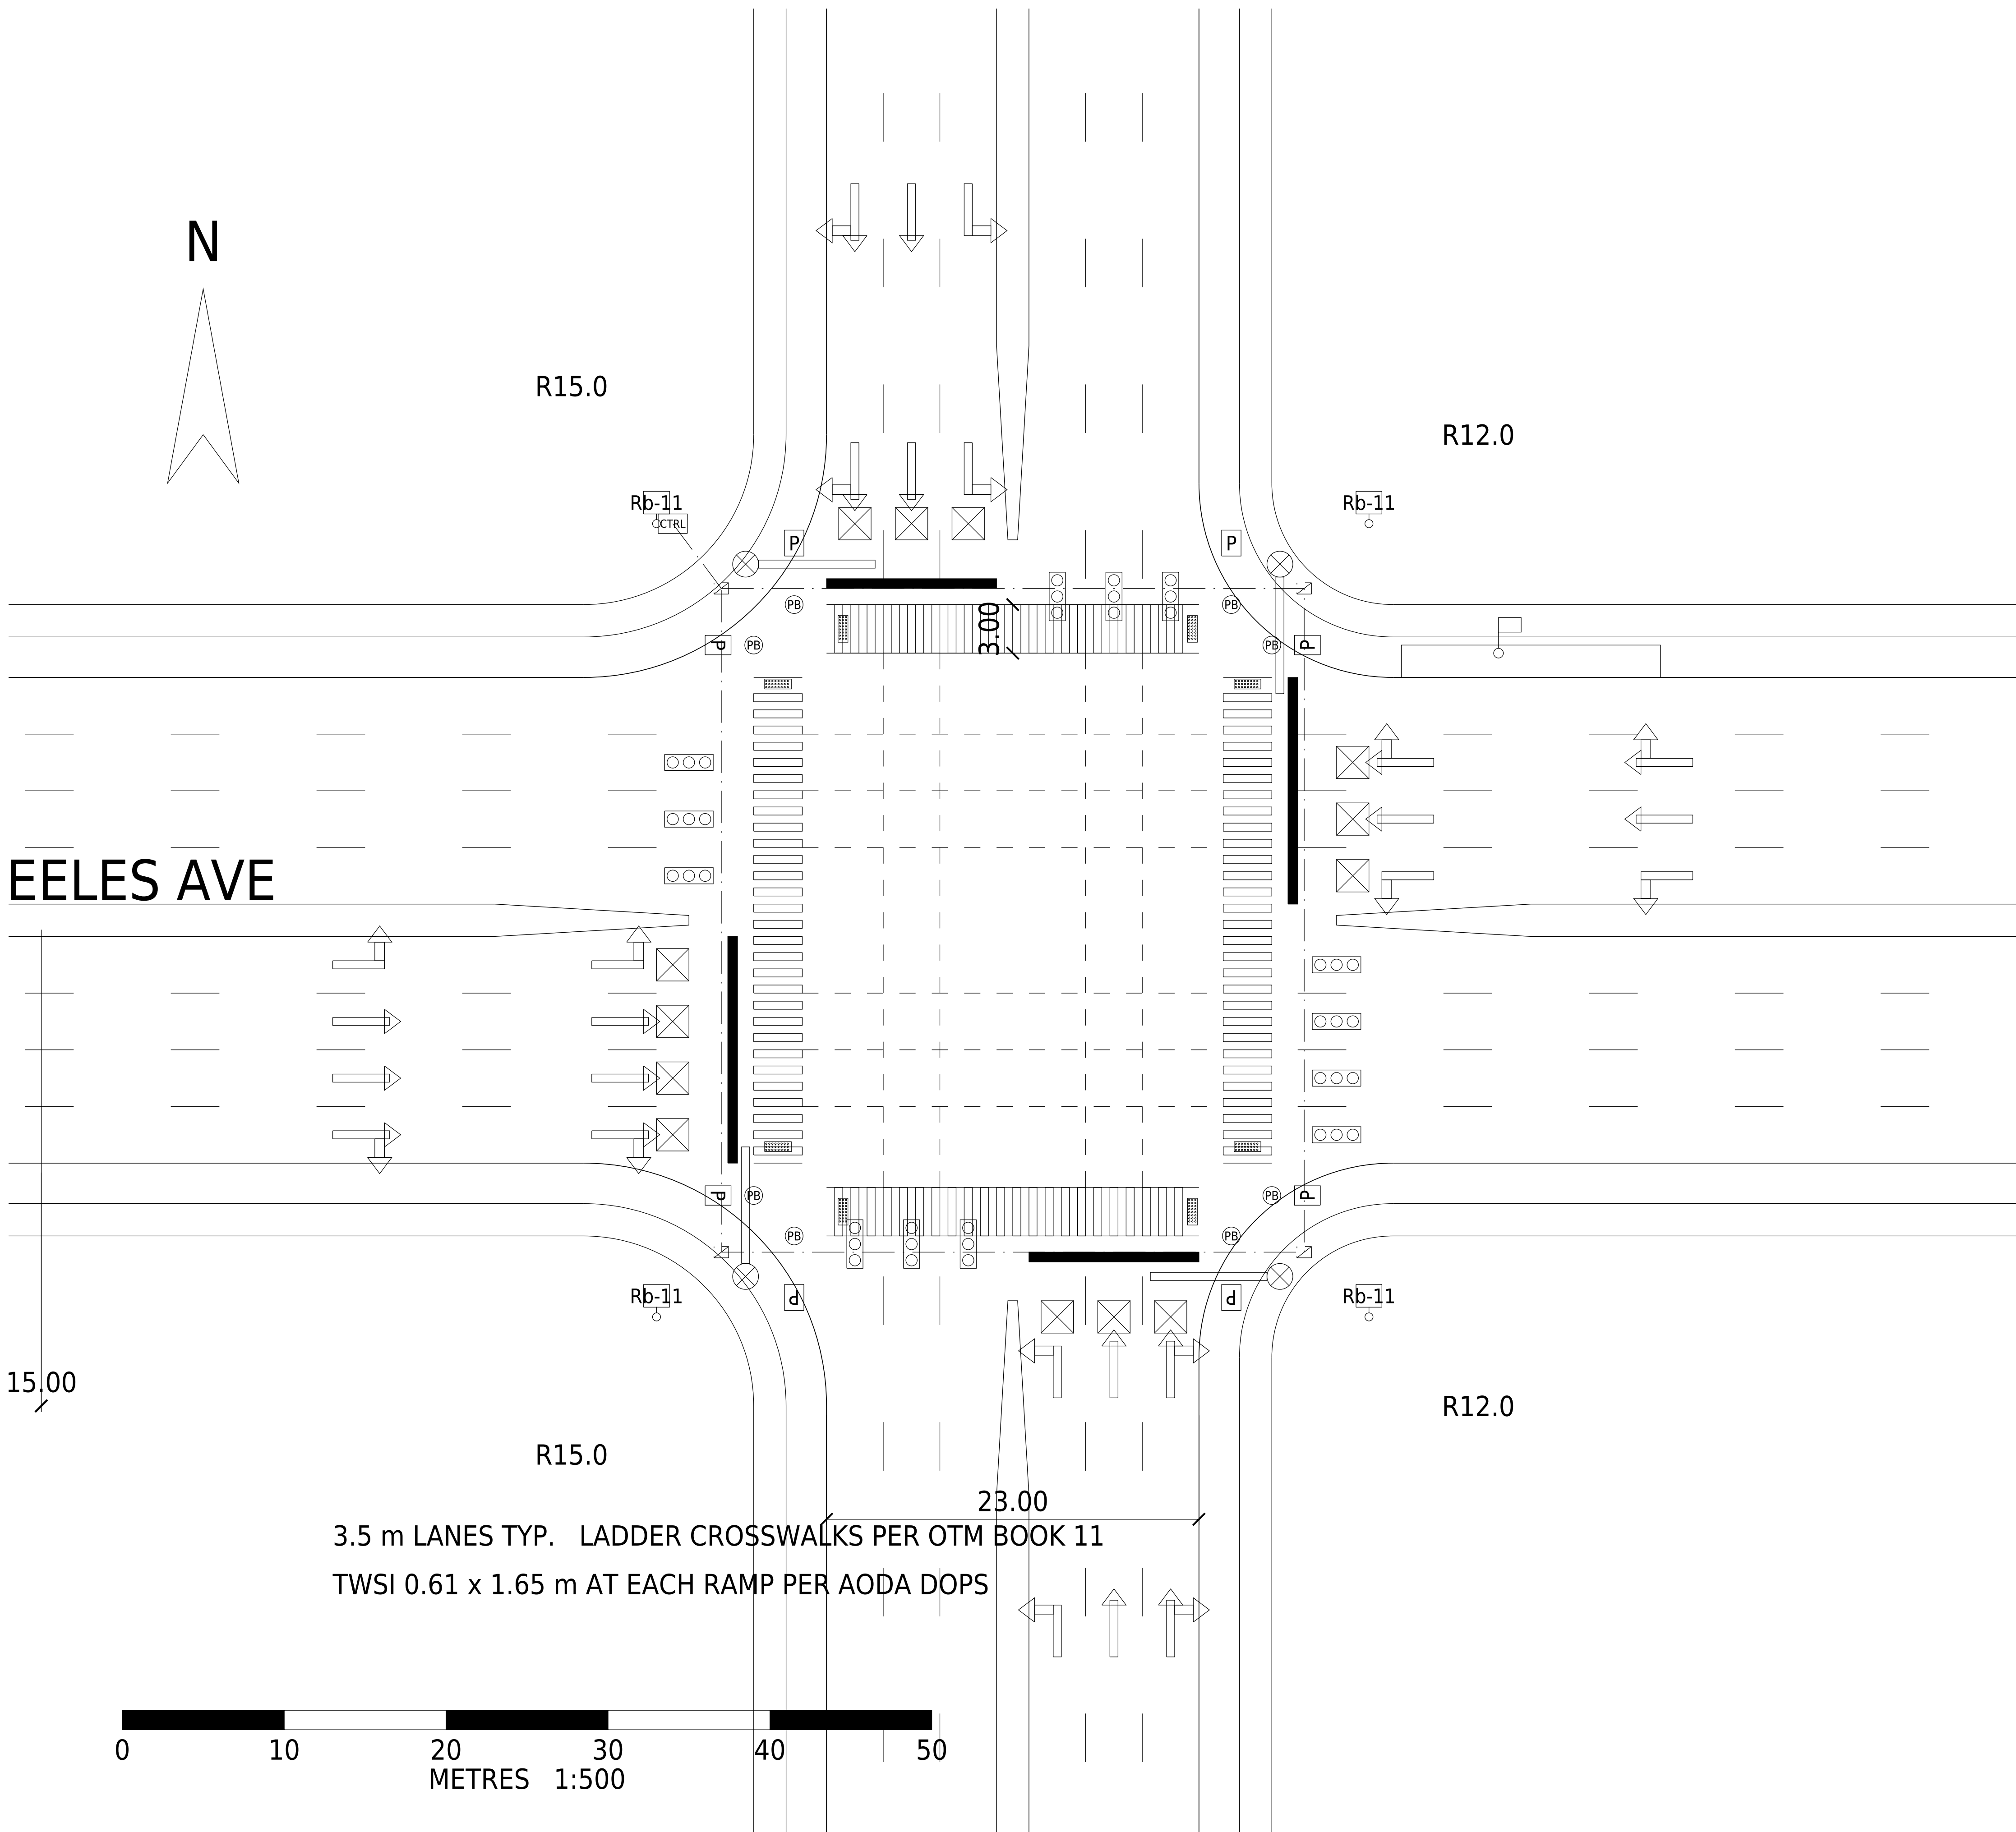

INTERSECTION IMPROVEMENT PLAN

GEOMETRIC LAYOUT, SIGNAL AND
PAVEMENT MARKING PLAN

LOCATION

STEELES AVE AT YONGE ST
TORONTO, ONTARIO PX 131

DEMAND

PM PEAK HOUR 16:45 - 17:45
4,909 VEH/H TMC 116429, 30 JUNE 2026

SIGNAL TIMING

130 s CYCLE, PROTECTED LEFTS
LOS D, 53.1 s CONTROL DELAY (HCM 6th)

REFERENCES

TAC GEOMETRIC DESIGN GUIDE
OTM BOOK 11 AND BOOK 12
AODA DESIGN OF PUBLIC SPACES

SCALE 1:500 ON A1 SHEET 1 OF 1

DRAWN BY M. KHALAJI
DATE AUGUST 2026

Lane configuration from OpenStreetMap tagging.
Corner radii and equipment positions assumed.
Base drawing, not a surveyed design.